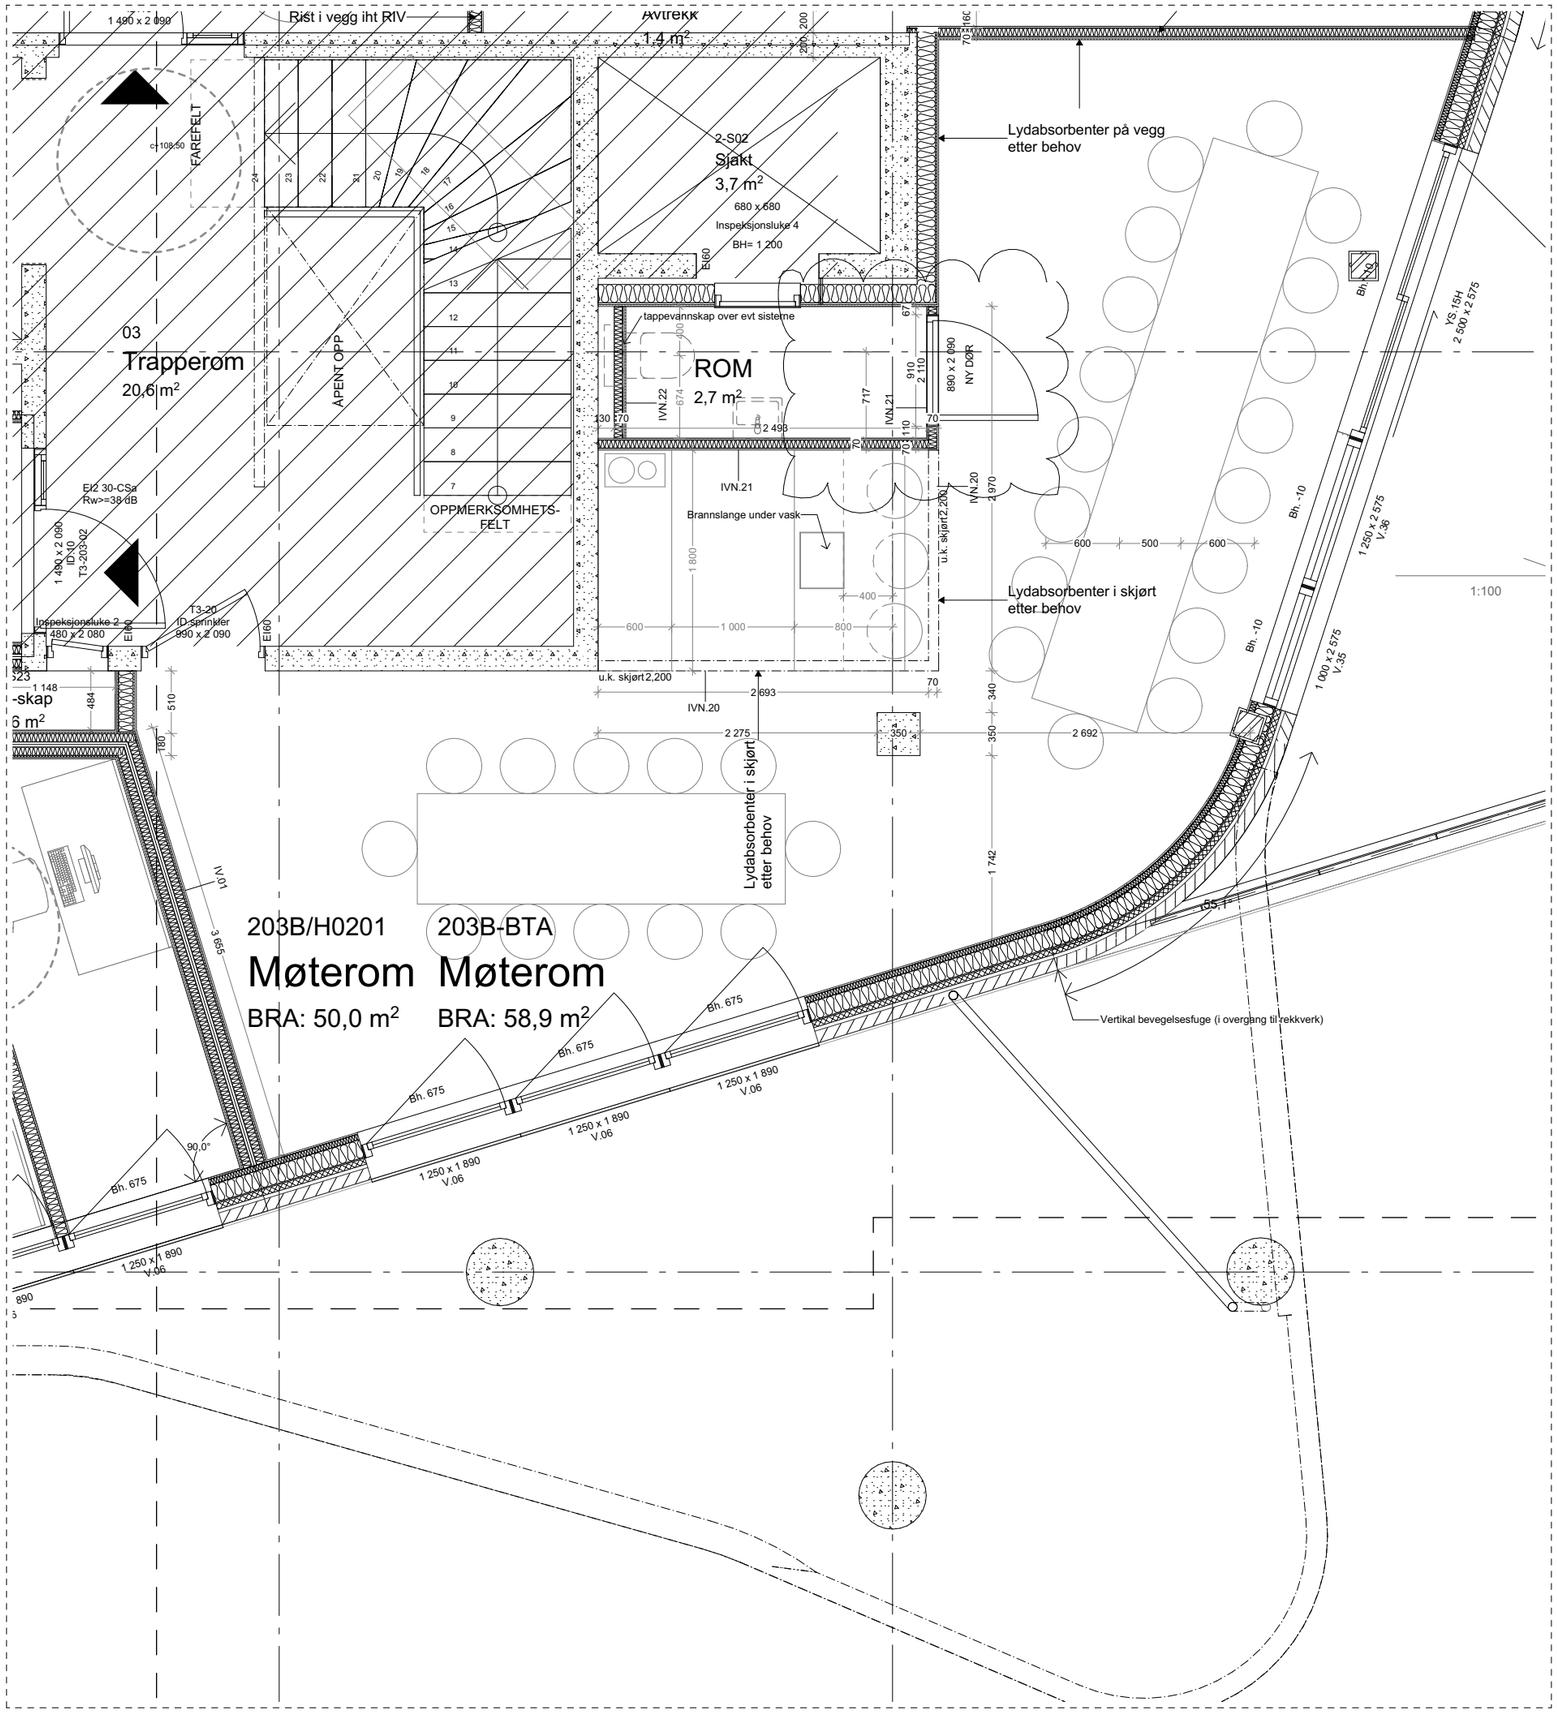

Beskrivelse overflater

Vegger:
Alle veggoverflater males Jotun 2500 Krydder iht. leietaker

Gulv:

Expona 4019 Weathered Country Plank (iht leietaker)

Dører:

Massivdører iht. plantegning, farge iht. leietaker

Belysning:

Iht. RIE

Utstyr:

Kjøkkeninventar, hyller og skap iht. leietaker / kjøkkenleverandør

Veggtyper

IVN.20 (70STENDER FOR INNKASSING/ PÅFORING)	83	13mm gipsplate, 70mm isolert stenderverk
IVN.21 (70STENDER, LYDKRAV 24dB)	96	13mm gipsplate, 70mm isolert stenderverk, 13mm gipsplate
IVN.22 (70STENDER, LYDKRAV 34dB)	96	13mm gipsplate, 70mm isolert stenderverk, 13mm gipsplate
IVN.31 (100STENDER)	126	13mm gipsplate, 100mm isolert stenderverk, 13mm gips

HENVISNINGER:

Tegning gjelder kun for innredning i næringslokale.

For generelle arbeidstegninger plan 2
- se A22-21/22/23/24/25

For himling, se Himlingsplan A26-203B

Rev.	Dato	Beskrivelse	Sign.	Kont.
H05	31.01.2022	rev dør til bakrom	MBJ	MKA
H04	07.01.2022	rev spek overflater iht leietaker	MBJ	MKA
H03	09.06.2021	rev planløsning for brannslange	MBJ	MKA
H02	06.12.2021	Endret inngangsparti, komplettering	MK	MBJ
H01	15.11.2021	Arbeidstegning	MK	CWE

Tegn. nr: A27-203B
Tittel: Næringslokale 203B
Rev.: H05

Tiltakshaver
WESSELKVARTALET AS

Arkitekt
VIGSNÆS+KOSBERG++ ARKITEKTER
Henrik Ibsens gate 100 / 0255 Oslo / Norway / Phone: +47 22 99 43 43 / e-mail: post@v-k-o.no / www.v-k-o.no / Org. no.: 976 867 868

Totalentreprenør
SV BETONG
Dreierveien 25 / 4321 Sandnes / Norway / Phone: +47 51 60 77 40 / e-mail: post@svbetong.no / Org. no.: 976 176 014

Prosjektnr: 522.15
Prosjekt: WESSELKVARTALET

GNR/BNR:
50/33 m.fl.
Adresse:
Bankvelen 4,1383 Asker

Status
ARBEIDSTEGNING

Tegningsdato: 10.11.2021
Tegningsskala: 1:50 (A3)

Tegn. nr: A27-203B
Tittel: Næringslokale 203B
Rev.: H05

31.01.2022