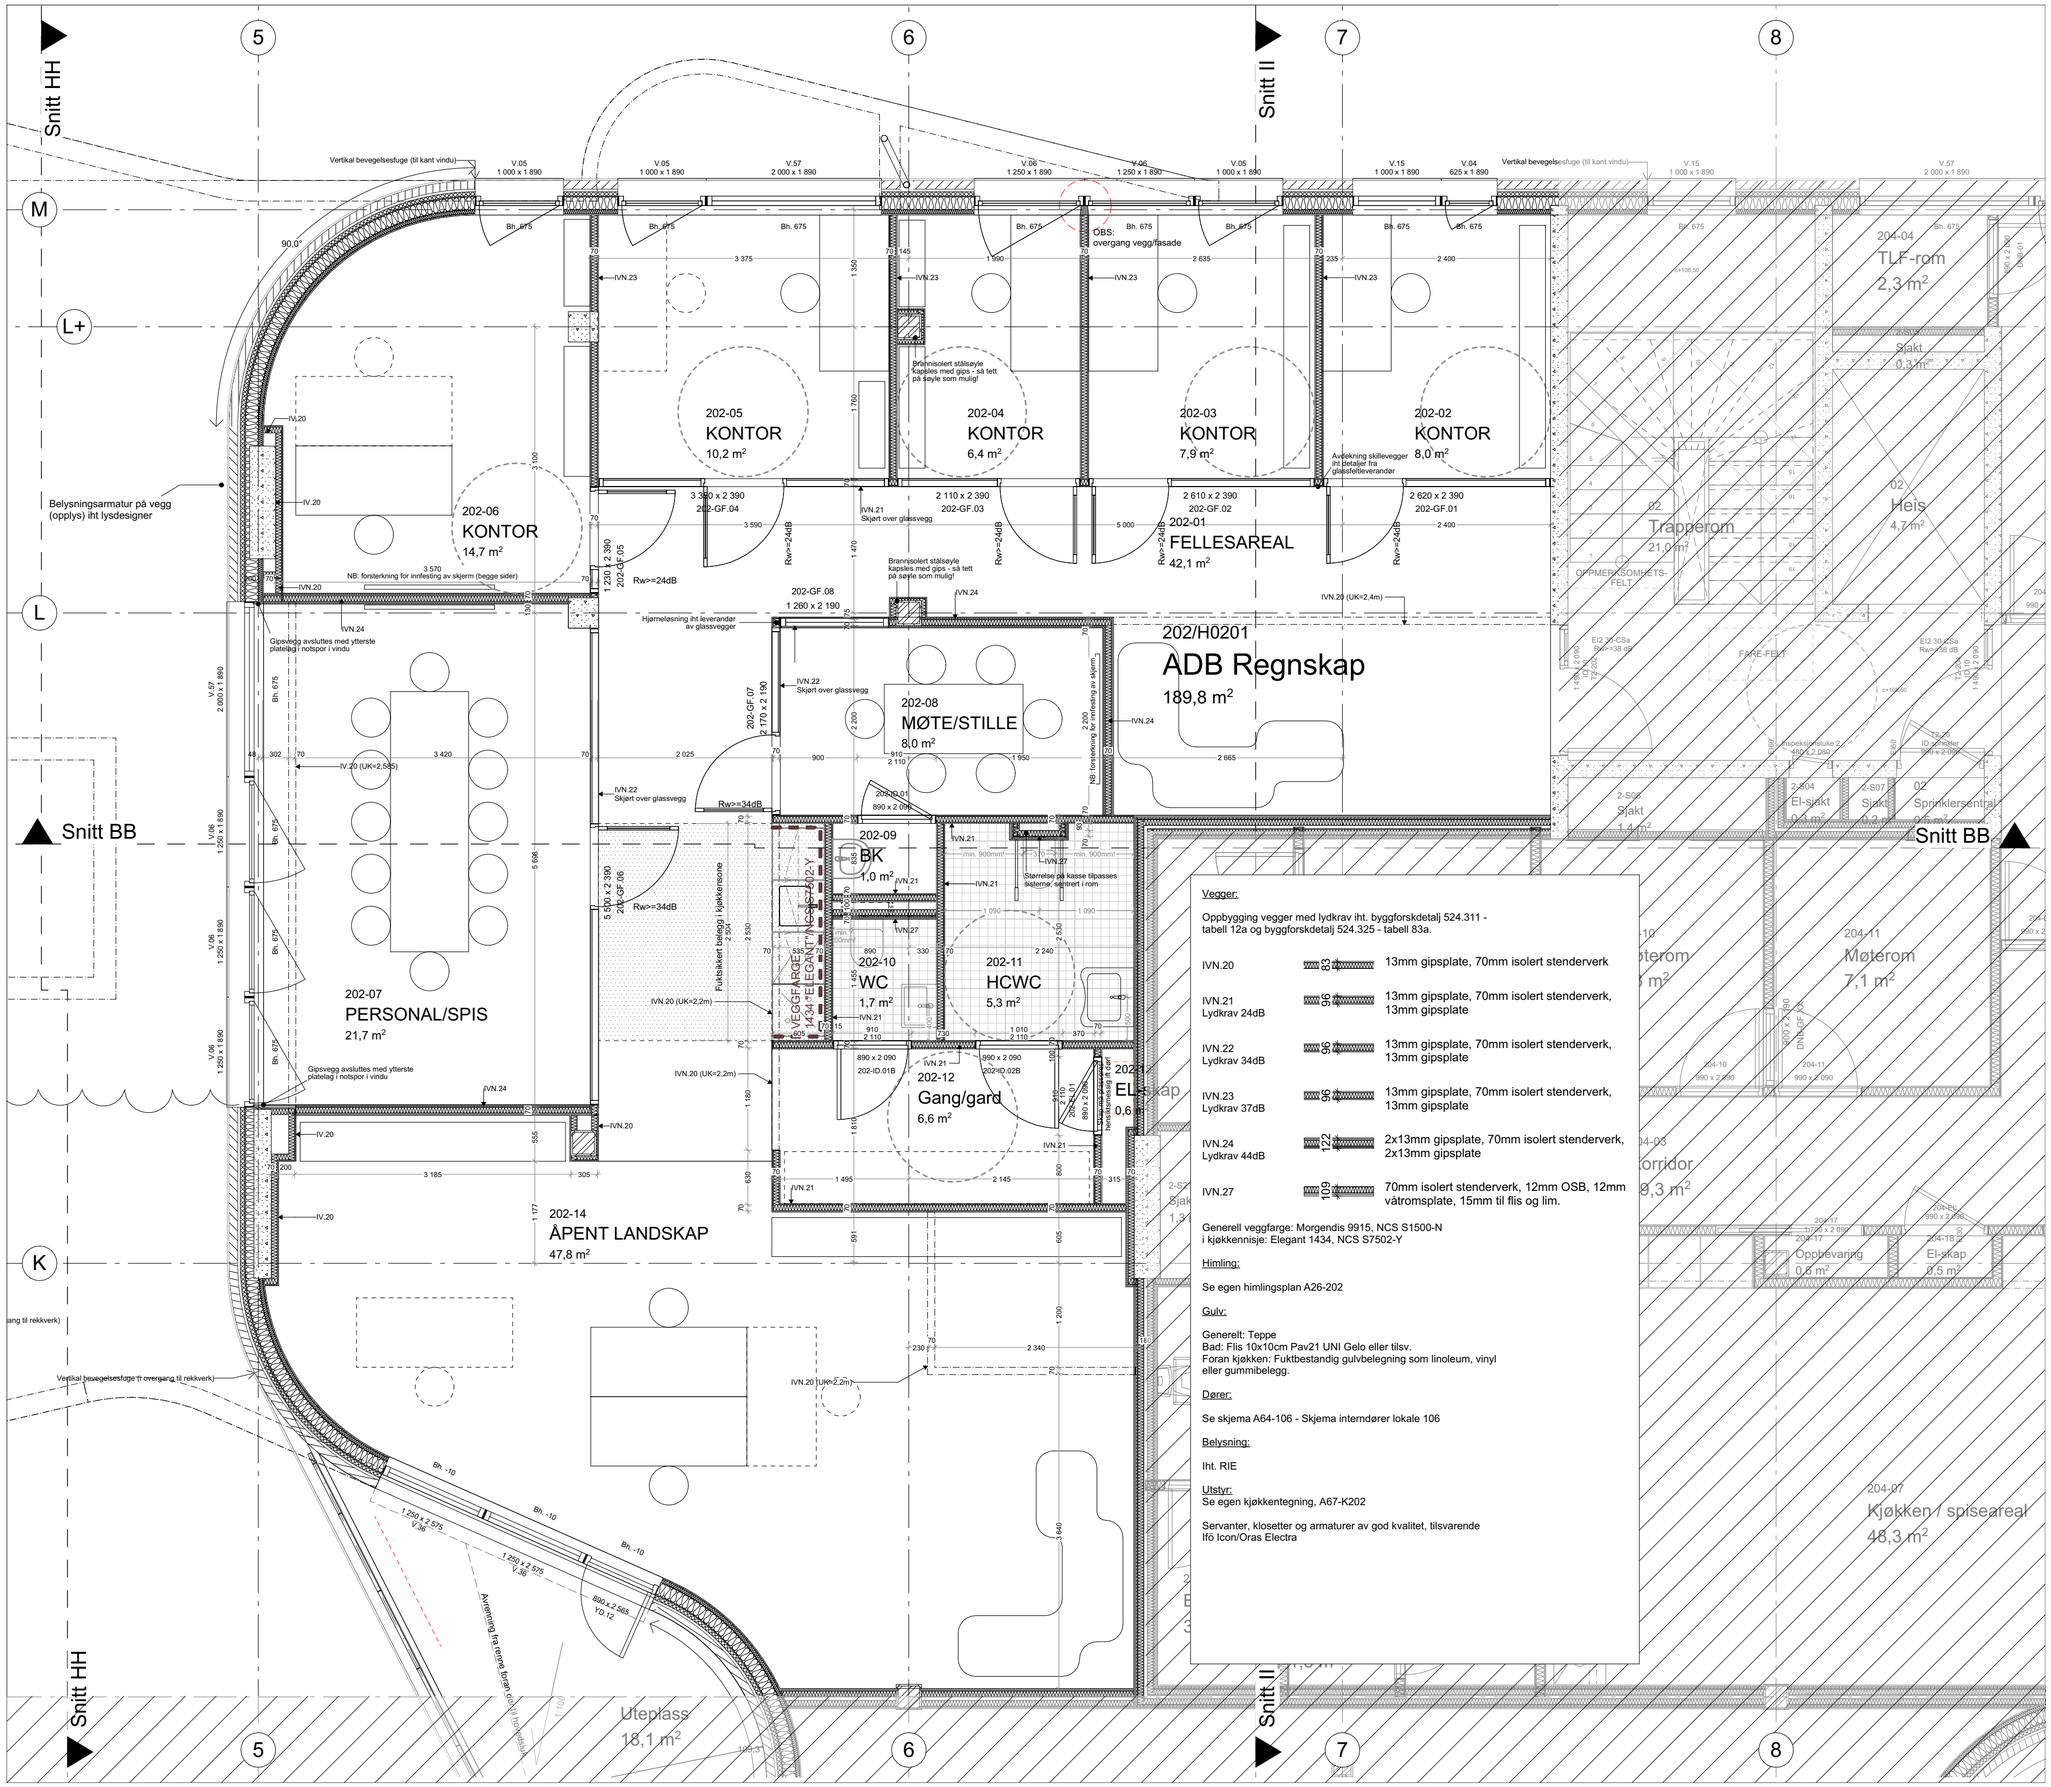

HENVISNINGER:
Tegning gjelder kun for innredning i næringslokale.

For generelle arbeidstegninger plan 2
- se A22-21/22/23/24/25

UK skjørt over glassfelt tilpasses høyder fra leverandør.
Skjema glassfelt/dører utarbeides av leverandør etter kontrollmål.
Avdekning/detaljering ved skillevegger hjørner iht leverandør av glassfelt.
Sortlakkerte profiler.

Rev.	Dato	Beskrivelse	Sign.	Kont.
H01	04.02.21	ARBEIDSTEGNING	MBJ	HVI

Tegn. nr	Tittel	Rev.
A27-202	Næringslokale 202	H01

N

- Takplan
- Plan 8
- Plan 7
- Plan 6
- Plan 5
- Plan 4
- Plan 3
- Plan 2
- Plan 1
- Plan U1
- Plan U2
- Plan U3
- Plan U4

Tiltakshaver
WESSELKVARTALET AS

Arkitekt
VIGSNÆS + KOSBERG ++ ARKITEKTER
Henrik Ibsens gate 100 / 0255 Oslo / Norway / Phone: +47 22 99 43 43 / e-mail: post@vi-ko.no / www.vi-ko.no / Org. no.: 976 867 866

Totalentreprenør
SV BETONG
Dreierveien 25 / 4321 Sandnes / Norway / Phone: +47 51 60 77 40 / e-mail: post@svbetong.no / Org. no.: 976 176 014

Leietaker
ADB REGNSKAP
Kontaktperson: May Elisabeth Karlsen // 92693367 // may@adbregnskap.no

Prosjektnr	Prosjekt
522.15	Wesselkvartalet

GNR/BNR:
50/33 m.fl
Adresse:
Bankveien 4, 1383 Asker

Status
ARBEIDSTEGNING

Tegningsdato	Tegningsskala
04.02.2021	1:50 (A2)

Tegn. nr	Tittel	Rev.
A27-202	Næringslokale 202	H01