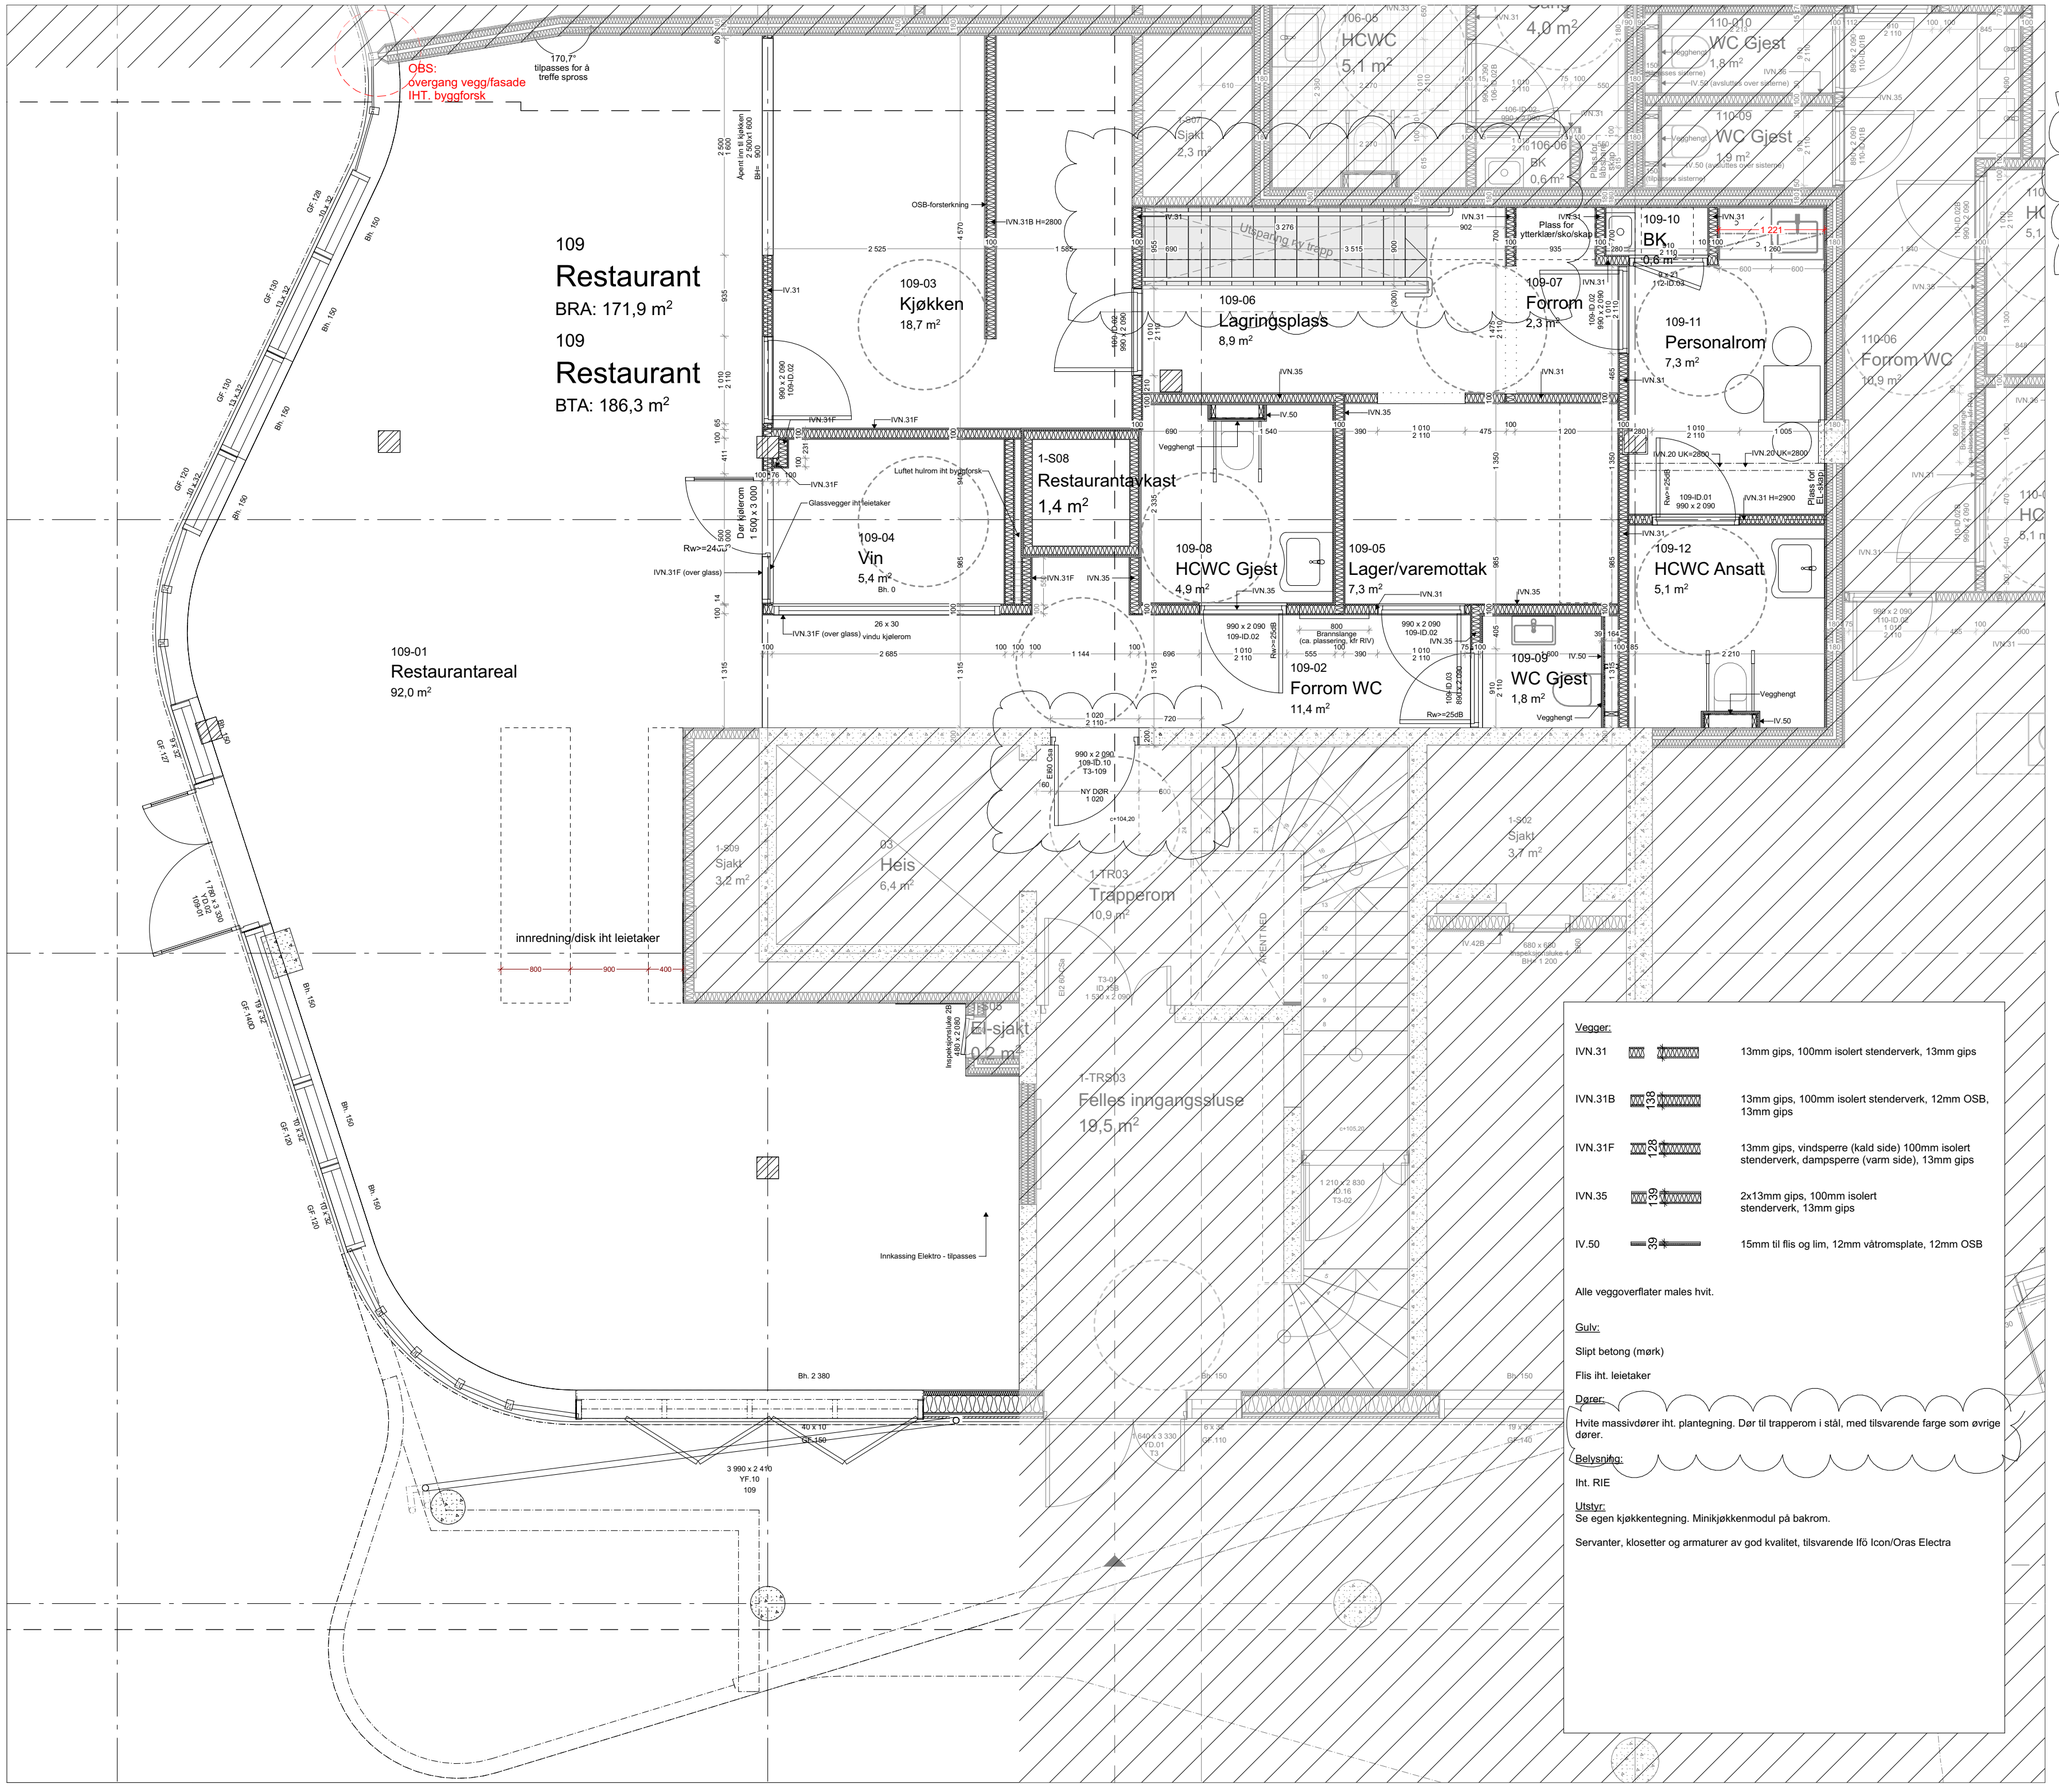


HENVISNINGER:
Tegning gjelder kun for innredning i næringslokale.

For generelle arbeidstegninger plan 1
- se A22-11/12/13/14/15

Se også himlingsplan A26-109, og skjema trapp A68-08. OBS: krav til sideplass ved dør mellom 109-06 og 109-03 må løses ved å fjerne dør eller ha automatisk åpning.

Kjøleromsvegger iht anvisninger i byggforsk.
Luftet hulrom må luftsirkulasjon.

Nye utsparinger i betong - kfr RIB!

Rev.	Dato	Beskrivelse	Sign.	Kont.
H03	16.02.22	Posisjon ny dør mot trapp, ny internttrapp	MBJ	MKA
H02	03.06.21	Luftet vegg mot sjakt	MBJ	HVI
H01	28.05.21	ARBEIDSTEGNING	MBJ	HVI

Vegger:

IVN.31	123	13mm gips, 100mm isolert stenderverk, 13mm gips
IVN.31B	133	13mm gips, 100mm isolert stenderverk, 12mm OSB, 13mm gips
IVN.31F	123	13mm gips, vindsperre (kald side) 100mm isolert stenderverk, dampsperre (varm side), 13mm gips
IVN.35	239	2x13mm gips, 100mm isolert stenderverk, 13mm gips
IV.50	20	15mm til flis og lim, 12mm våtromsplate, 12mm OSB

Alle veggoverflater males hvit.

Gulv:

Slipt betong (mørk)

Flis iht. leietaker

Dører:

Hvite massivdører iht. plantegning. Dør til trapperom i stål, med tilsvarende farge som øvrige dører.

Belysning:

Iht. RIE

Utstyr:
Se egen kjøkkentegning. Minikjøkkenmodul på bakrom.

Servanter, klosetter og armaturer av god kvalitet, tilsvarende Ifö Icon/Oras Electra

Tegn. nr
A27-109

Tittel
Næringslokale 109

Rev.
H03

N

- Takplan
- Plan 8
- Plan 7
- Plan 6
- Plan 5
- Plan 4
- Plan 3
- Plan 2
- Plan 1
- Plan U1
- Plan U2
- Plan U3
- Plan U4

Tiltakshaver

WESSELKVARTALET AS

Arkitekt

VIGSNÆS + KOSBERG ++ ARKITEKTER

Henrik Ibsens gate 100 / 0255 Oslo / Norway / Phone: +47 22 99 43 43 / e-mail: post@vi-ko.no / www.vi-ko.no / Org. no.: 976 867 866

Totalentreprenør

SV BETONG

Dreierveien 25 / 4321 Sandnes / Norway / Phone: +47 51 60 77 40 / e-mail: post@svbetong.no / Org. no.: 976 176 014

Leietaker

TAPAS POR FAVOR

Kontaktperson: Benedicte Nilsen // 90835065 // benedicte@crianza.no

Prosjektnr
522.15

Prosjekt
Wesselkvartalet

GNR/BNR:
50/33 m.fl

Adresse:
Bankveien 4, 1383 Asker

Status
ARBEIDSTEGNING

Tegningsdato
28.05.2021

Tegningsskala
1:50 (A2)

Tegn. nr
A27-109

Tittel
Næringslokale 109

Rev.
H03